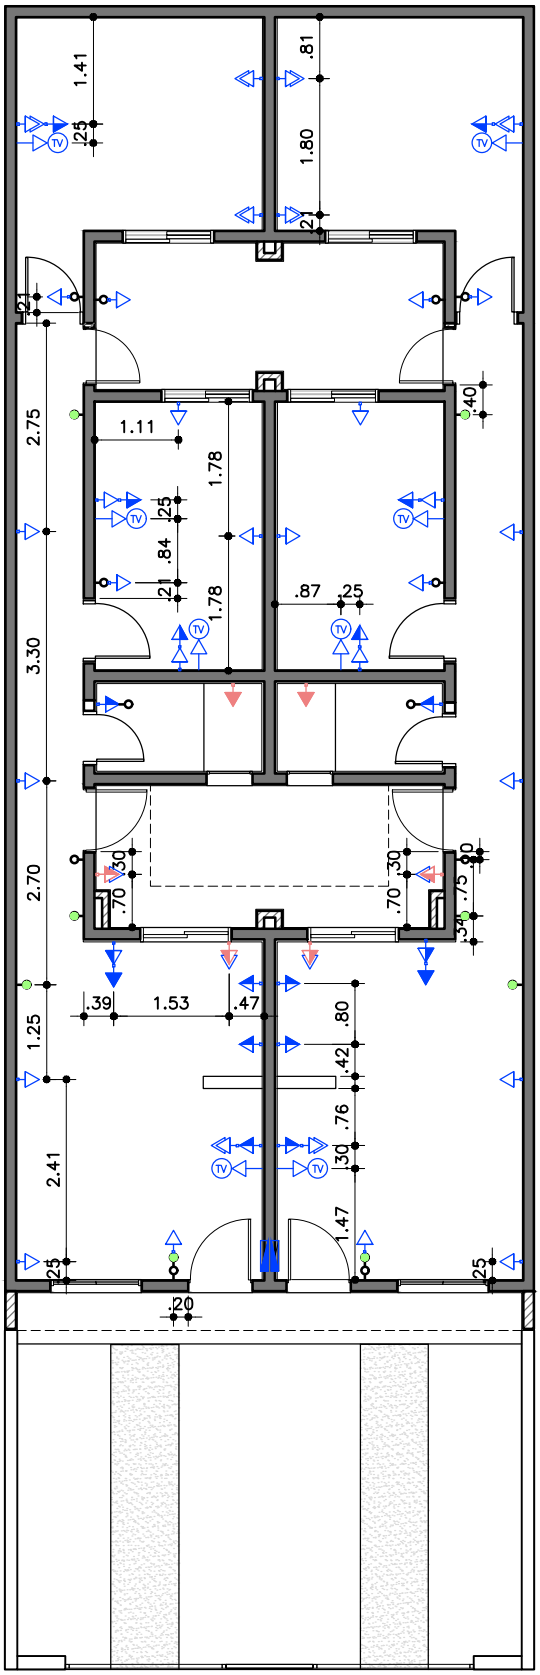

LEGENDA ELÉTRICA	
	TOMADA SIMPLES 127V - BAIXA
	TOMADA DUPLA 127V- BAIXA
	TOMADA SIMPLES 127V - MÉDIA
	TOMADA DUPLA 127V - MÉDIA
	TOMADA SIMPLES 127V - ALTA
	TOMADA DUPLA 220V+127V - MÉDIA
	DADOS / INTERNET / TELEFONIA
TV	PONTO TV / HDMI
	INTERRUPTOR SIMPLES
	INTERRUPTOR PARALELO
	QUADRO DE DISTRIBUIÇÃO DE FORÇA

DMSL arquitetos

cliente | **TEV CONSTRUTORA E INCORPORADORA LTDA.**
endereço | **RUA TUMIARU, 88 - VILA MARIANA - SÃO PAULO/SP**

etapa projeto | **PROJETO EXECUTIVO**
desenho | **PLANTA ELÉTRICA**

folha | **00** escala | **1:100** data | **NOVEMBRO/2023** rev. | **R01**